



迷いの路、始まる縁

01 コンセプト

現代では人と人が出会い繋がりやすくそれが当たりまえになりつつある。ネットで離れていても繋がれる。その土地に長くいると出会いもいくつかあるだろう。だが、意図した出会いが当たり前になり連続すると偶然を逃してしまうことがある。現代は意図した出会いが増えるからこそ偶然は貴重であり大切なものになるだろう。普段行かない土地・店・道、そうした場所で起こる一瞬の出会いを逃さずものにできれば生活が豊かになるのではないだろうか。

02 提案

偶然を誘発するためには人々が意図せず出会うことが必要である。また、人が入れ替わることで新たな人とひかれあふ。本提案では動線を迷わせる計画とし偶然を引き起こす。一ヶ月ごとに去る人来る人が絶えず入れ替わる、そんな住宅を構想する。迷いは意図的ではなく偶然を引き起こす。偶然は出会いの起点となる。

03 偶然を引き起こす 迷いの路

① 目印を少なくする
どの曲がり角も同じ
ような景色にする。

② Y字路にする
角をなくし、曲がった
感覚を狂わせる。


04 ダイアグラム

住宅の部屋をLDK、寝室に細分化することで生活の一部に路を通る時間ができる。また、ランドリー、風呂、多目的に使用するLDKを共用とすることで、人と人が出合いやすくなる。

① 共用部を敷地の中心に集める

② 共用部の周りにLDKなどの個室を配置する

③ できた隙間に路を入れる

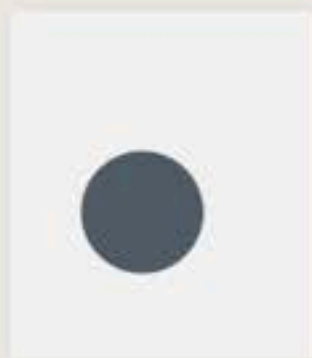

他族団欒 ～2Fの乾杯～

他者と“家族になる”建築

同じ空間・同じ時間を共有するが偶然の出会いを深い関係に…
リアルを蔑ろにするな「Face to Face」で乾杯を

～問題提起～

最近ではご近所付き合いは減少し、他者とコミュニケーションを築く機会が失われつつある。さらにSNSの普及により偶発的な出会いが生まれにくく、人と人との関係が深まりにくい状況にある。

その結果、人が空間に滞在し関係を築く機会が減少する。空間は単なる通過や機能として消費される傾向にある。

空間は人と人をつなぎ、関係を生み出す役割を持つものであるが、その機能が十分に発揮されていない。


～解決案～

本計画では、人と人との関係が自然に生まれる空間の機能に焦点を当てた計画とした。

同じ空間・時間を共有できる場を各階に段階的に配置することで、人々の行動から偶発的な出会いが生まれる構成とし、主となる2階には共用空間を設け、人々が滞在し、交流が生まれる中心の場とした。

これにより、日常の中で自然な関わりが生まれ、他者との関係を築ききっかけを創出する。

「建築は人を導く力を持つ」

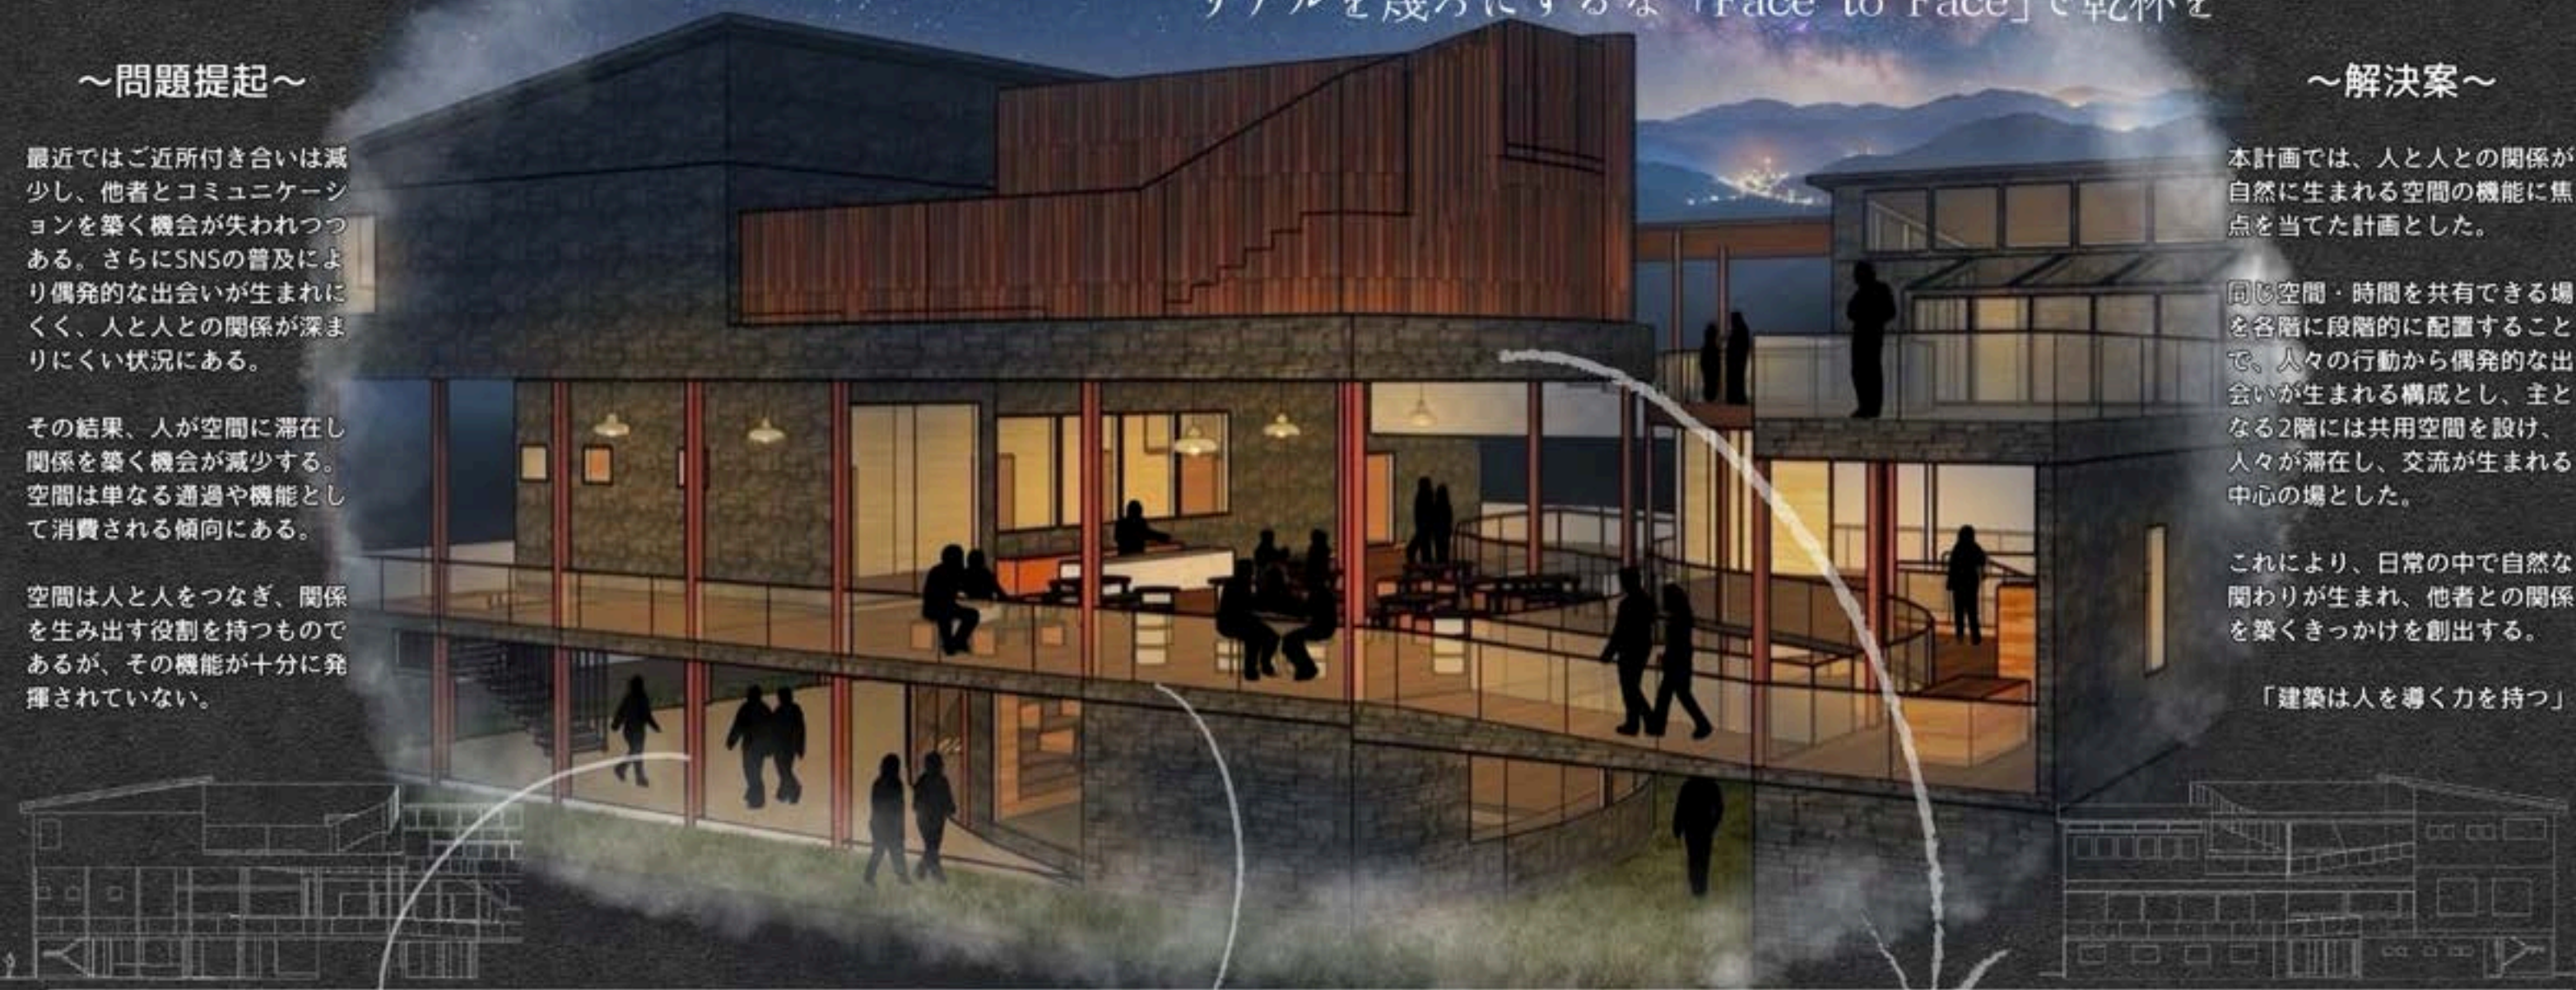


1F

2F

3F

1F みんなの玄関

この建物は2棟が並んで建てられているため真ん中に東西を繋ぐ通路が出来ている。通り抜ける時賑やかな声が聞こえ、足が止まり、新たな交流の玄関に足を踏み入れる。1階は誰でも入りやすいスペースが多く来る人を拒まない。

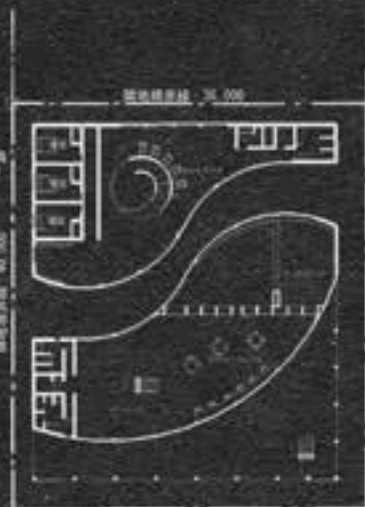

2F 交流の酒場

食事がメインのこの階層では壁で囲まれている部分が少なく、多くが屋外又は半屋外のスペースとなっている。南側には騒げる賑やかな場所、北側には静かに飲めるBARがある。南側の個室には最低限の設備だけにしており必然的に交流の機会を産む



3F 癒しの空間

南側に温泉施設を設けて食後にそのまま入浴することで2階の酒場で仲良くなった人とそのままお風呂でより仲を深めることができる。又、小上がりの和室を設けることでリラックスできるスペースも完備している。北側にはランドリールームとサンルームを設けており、雨天問わず洗濯することができる。





人々は徐々に分散し、
独立して暮らし始める

日々織々

徐々に集まった
暮らし方へ

徐々に独立した
暮らし方へ


人々は徐々に固まり、
共同して暮らし始める

問題提起


現代の家族は血縁関係で結ばれ、1世帯1住居が当たり前となった。しかしそれと同時に、隣人との間に物理的・心理的な壁を生みだし、家族以外との関係構築を難しくしてしまっている。だからこそ、「脱家族」という概念が必要ではないだろうか。

設計趣旨

私は、「家族が変化し続ける」ことを脱家族と捉えた。人は独立と共生、その2つを繰り返すなかで関係性の新たな形を見いだす。1年を通じて共同生活と独立した生活を交互に行うことで、人と人との距離の押し引きを生みだし、脱家族＝新たな家族の形を提案する。

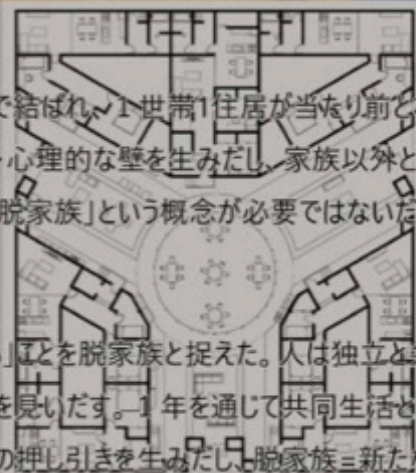


変化する7世帯の暮らし方

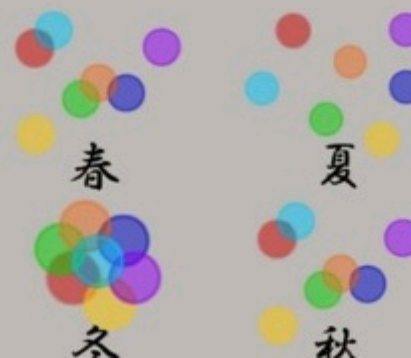

1年という年月をかけて、
共同と独立を繰り返す。

コンセプト

四季に応じた水位の変化が、居住空間と人の暮らしを変えていく。

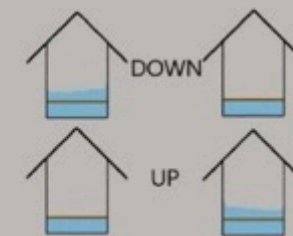

片方のエリアの水位が上がる
と、もう片方のエリ
アの水位が下がる。

暮らしの先に

1年間という時間の流れのなかで、人々は家族のあり方や、人との距離感について、少しずつほどこけていく。やがて血縁としての家族に縛られることなく、それぞれの関係性が、日々の暮らしの中で静かに織り成されていく。

核家族の脱却 ～人々の群れ観察～

問題提議

現代日本では核家族が中心となり、生物的本能である群れる生活からかけ離れつつある。

プライバシーを守ることにより注力する現代、他人との関りが少なくなり、家と家は壁で仕切られ、横にどんな人が住んでいるのか分からない。

分からないから身を守る。プライバシーを守るため閉鎖的になる。

コンセプト

閉鎖的になる原因として、壁があるからプライバシーを守ろうと消極的になり視線を遮る。そこで敢えて、間仕切り壁を腰壁にすることでプライバシーを無くし、消極性を無くす。


また視線が広がり、空間が広く見えることで交流も活発となり、高低差を作ることで見え方が変わるという楽しさも生まれるようにした。

そして段差は本能に問いかける仕掛けとして機能する。人の上に立ちたいという本能を強く持つ人はより高い所に行く。本能を刺激する建築を提案する。


住んでいる人が
立っている目線



通り庭を通行している
地域の人の目線

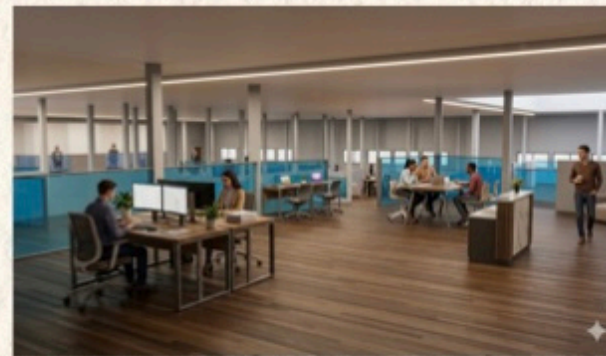


体を洗い終えて風呂につかるときに立った目線

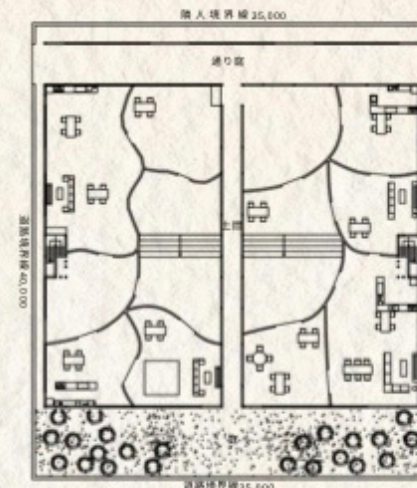

1F

暮らす全員が家族になる空間


この空間は視線をさえぎる壁がなく開放感がある。視界が広がっているため人の気配が常に感じることが出来、日々関わる集まりを変えながら生活をしていく。また通り庭を設けることで敷地を迂回することなく反対の道路に出ることが出来、通る人との関りも持つことが出来るため地域の繋がりを持つことができる

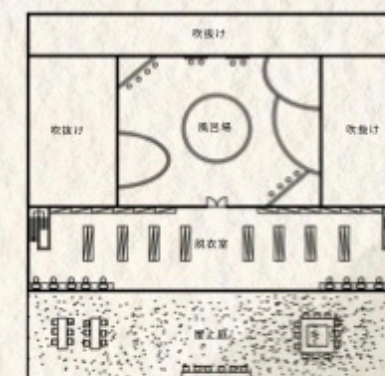

2F

男女の隔たりがない風呂場

すべてにおいてオープンにするための空間にする。
男女を分けると見えない壁が出来。そのため壁を取っ払うため混浴にすることで性別関係なく関係を深めることが出来る。また3方向に窓を設けることで風呂にいる人の会話や生活音を聞くことが出来るため1Fにいる人も回は分かれているが、人とのつながりを感じることが出来る

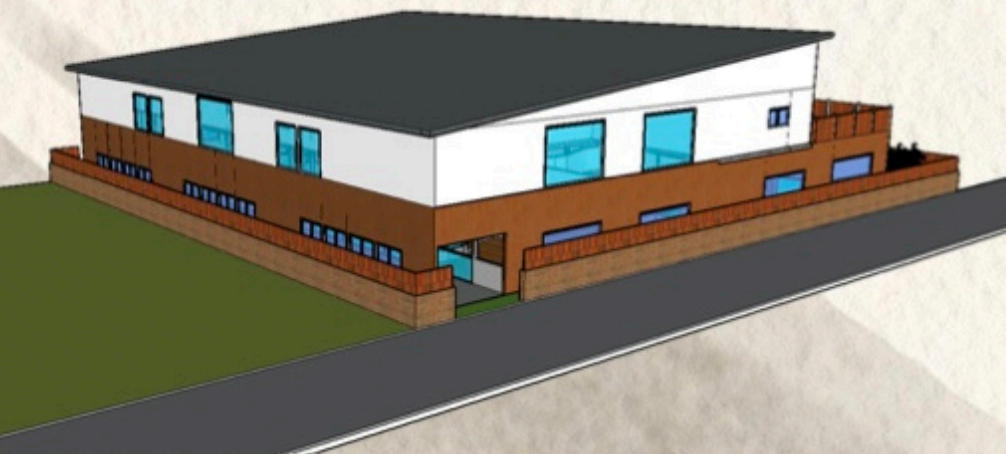

ただいまの庭 ~挨拶がつなく地域と暮らしの庭~



設計趣旨

「ただいま」は、自分の居場所を再確認する言葉だ。しかし、親しくない相手には、その言葉は出にくい。見知らぬ人に「おかえり」と言われても、思わず「こんにちは」と返してしまうように、言葉は関係性の距離によって変わってしまう。

核家族化が進んだ住環境では、帰宅は閉じた動線で完結し、顔を合わせる機会がなければ、関係も言葉も生まれにくい。

本計画では、7世帯の敷地に共有動線と余白を設け、地域住民も中庭を通りに抜けなくなる構成とし、挨拶が自然に交わる距離をつくる。


大樹を核に鳥の巣のような住戸が囲み、通り庭や回廊を通して人の気配を感じながら帰ることで、安心感と帰属感のある「帰る場所」を目指す。

「こんにちは」が、いつか「ただいま」に変わる。



「こんにちは」、いつか「ただいま」に変わる

柔軟な住まいの提案

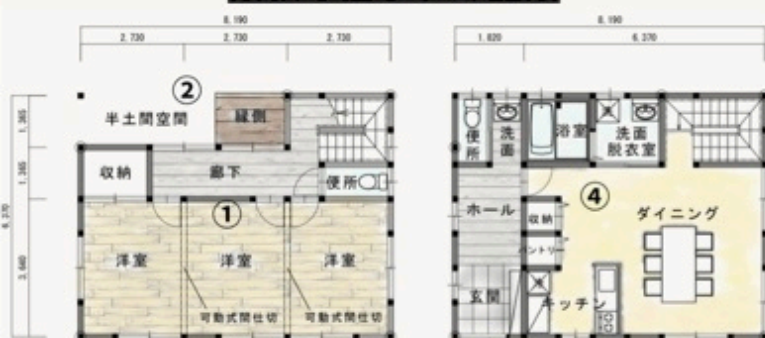

1階平面図 S=1:100

2階平面図 S=1:100

①可動式間仕切による可変空間
1部屋から3部屋へ。自由に変化する洋室。
・個室化：子供室2室と寝室1室として独立
・一体化：大きな1部屋として、映画鑑賞や趣味の部屋へ。
・適応：住む人の人数やステージに合わせて、無駄なく使い切る。

②内外をつなぐ半土間と縁側
暮らしが街に染み出す場所。街との緩やかなフィルターとなり、家の中にいながら外の気配を感じ、外の中にいながら家のくつろぎを享受する。




③2階玄関と回廊がつくる「気配」

あえて玄関を2階に配置。回廊を通して住宅に向かうことで自然と家族、他者の気配を感じられる。回廊という公的な空間を介し、意図的に「ただいま」を発生させる。

④「団楽」を再定義するキッチン&ダイニング

従来のリビングルームを廃し、キッチンとダイニングを中心に据える。ゆったりとした共有リビングは住民同士が自由に集まれる場。

01-動線ダイヤグラム 1階

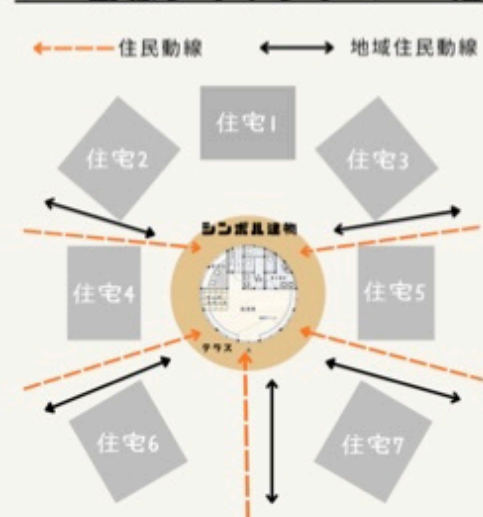

・住民は必ずシンボル建物の外階段を上がり、2階の玄関から住居に入る
・地域住民は必ず中庭を通して別の通り庭に行く

01-動線ダイヤグラム 2階



・回廊を通じて各住宅を行き来でき、顔を合わせることができる
・共有部では住民が好みに使い方を決められる
・各家族が共有リビングに集まることで自然と交流生まれる

02-空間グラデーション



境界を壁ではなく「層」にすることで、関係が緩やかに生まれる




03-時間帯による関係性

朝	夕方	夜
中庭・前庭	回廊・中庭・共用部	住戸・個室
・出勤動線が中庭で重なる ・軽い会釈が生まれる ・子供達が複数の大人に見送られる ・「いつてらっしゃい」が行き来する	・帰宅動線が緩やかに重なる ・子どもの笑い声が響く ・誰かが中庭や土間に滞在する ・「ただいま」が交差する	・個の時間に戻る ・共有部の灯りだけ残る ・強制しない ・共同体に回収しすぎない
家族機能の分散が最も見える時間	「ただいま」が最も起きやすい時間	個の時間を保つ時間


各家族 → 七世帯 → 地域へ

大樹と鳥の巣

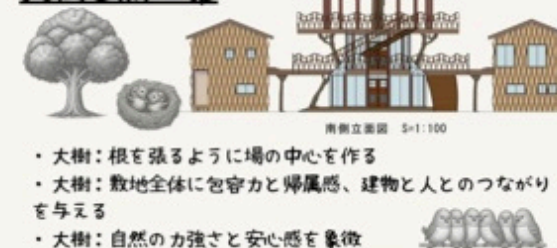

・大樹：根を張るように場の中心を作る
・大樹：敷地全体に包容力と帰属、建物と人とのつながりを与える
・大樹：自然の力強さと安心感を象徴
・鳥の巣：枝を重ねるように住戸を包み込む
・鳥の巣：外と内のあいだにやわらかな境界をつくる
・鳥の巣：自然との調和と安心感や有機的な美しさがある

地獄組

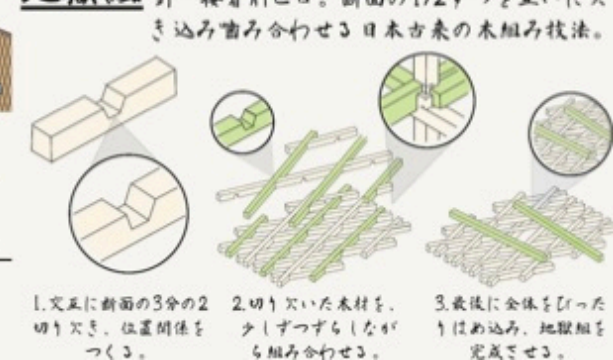


隣人の声で目が覚める
朝早くから元気だと思いつつリビングに降りて朝日を浴びる
通り庭にある洗面所で顔を洗う
後ろからAさんとBさんが通り挨拶をした
まだ喋っていて盛り上がっている
朝ごはんを食べる準備をした
朝ごはんを食べているときにCちゃんとDくんが通った
元気に挨拶をしてくれて今日も頑張ろうとやる気が出た
家を出て通り庭を通り「行ってきます」と挨拶をした



ケの日の通り庭では通学・通勤の隣人が通り
日常生活でも交流が生まれる



ハレの日では通り庭が
大きな土間空間となりリビングとなる

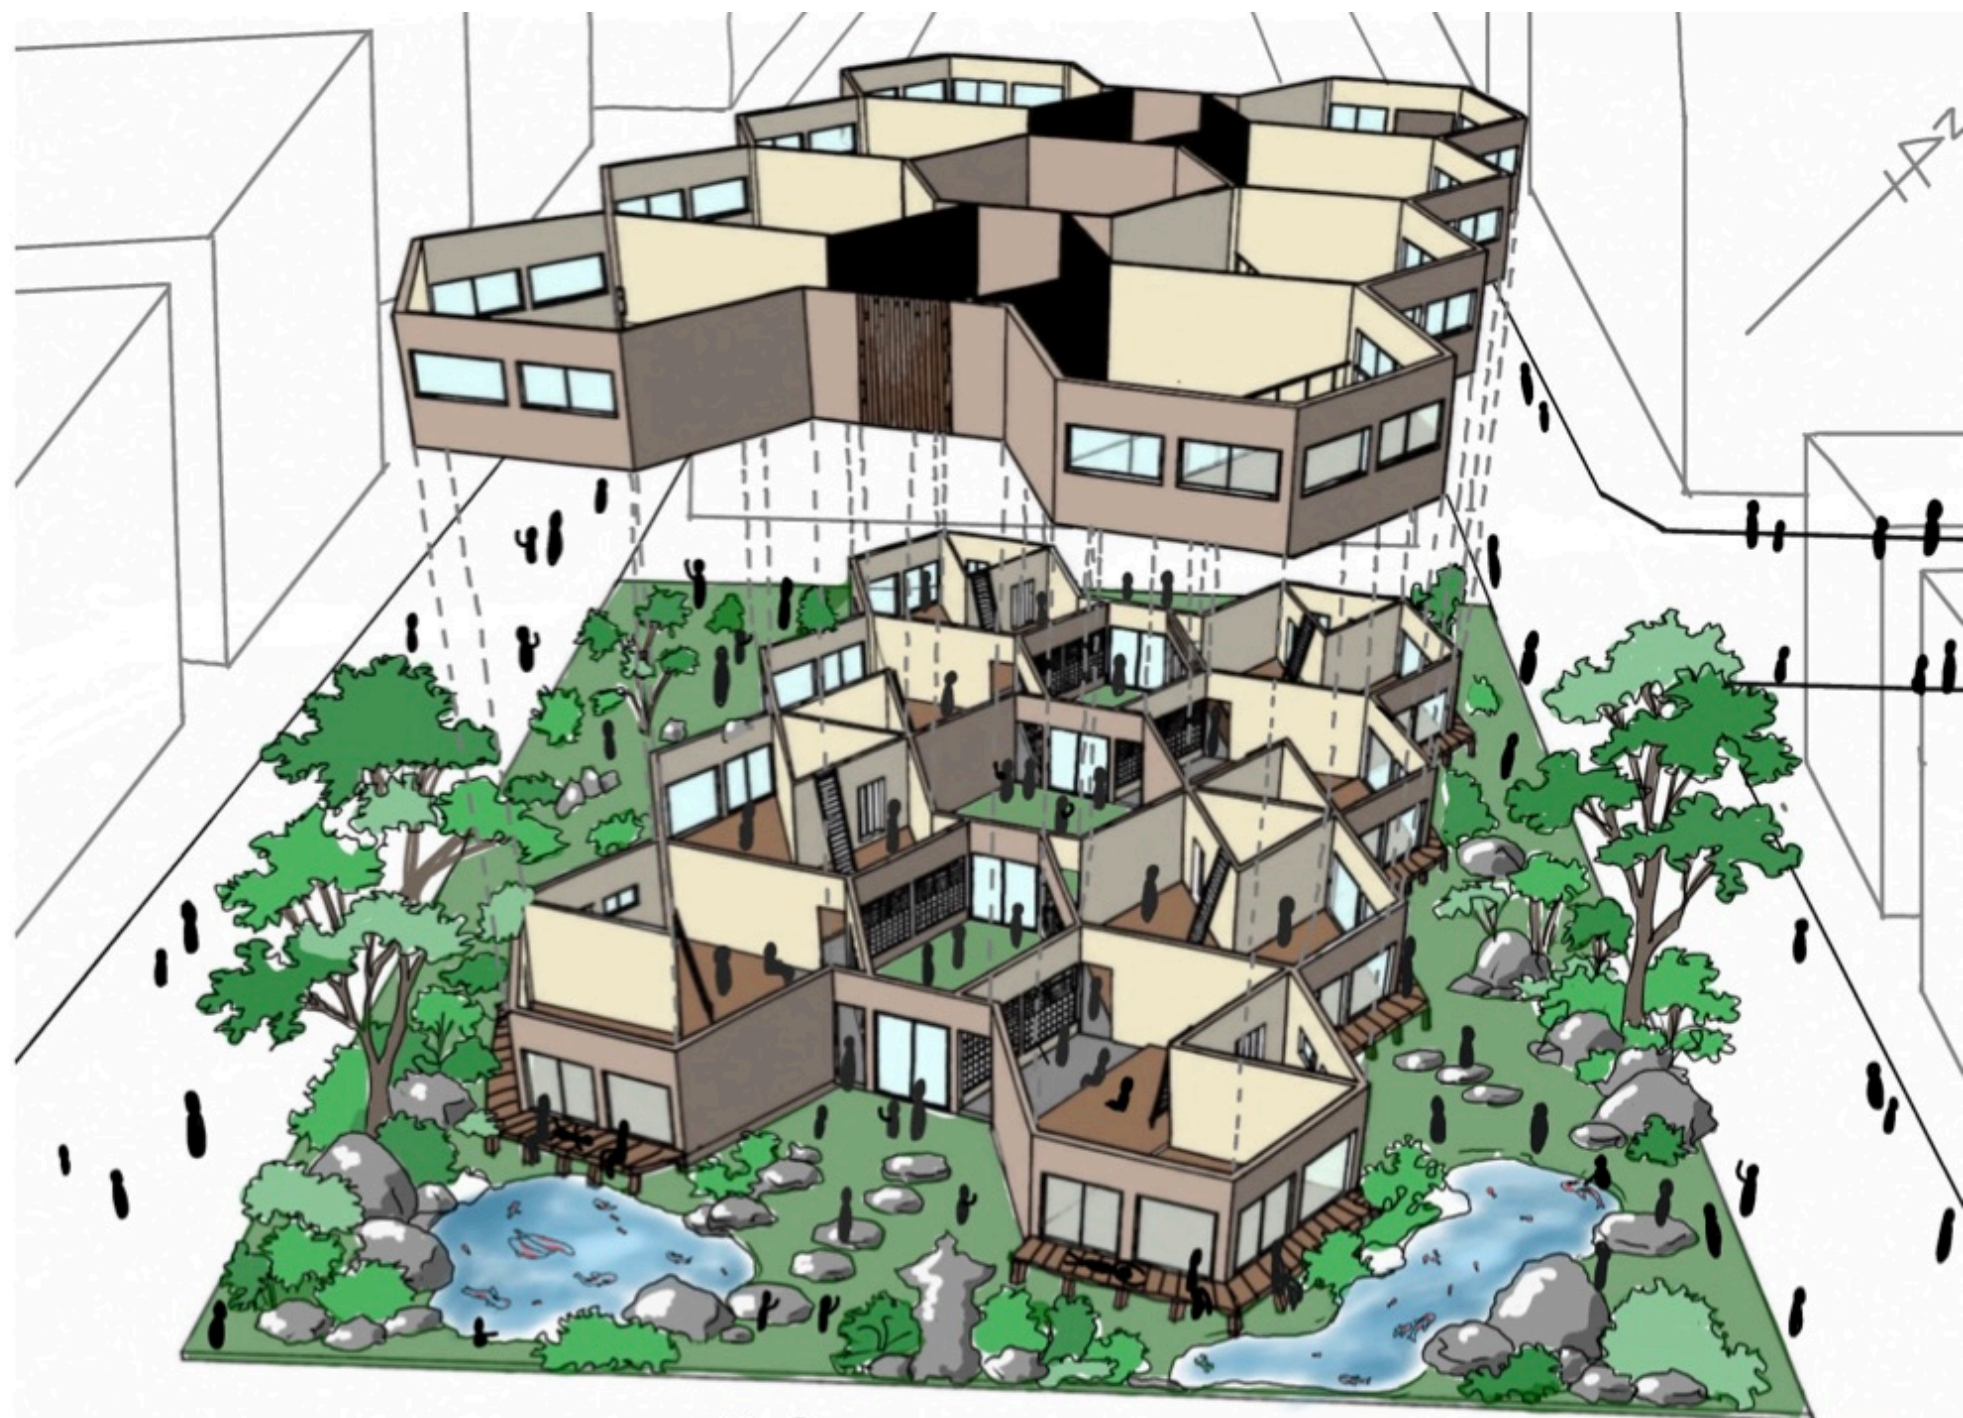

ハレとケを紡ぐ



本計画では通り庭を軸として空間のハレとケが変化する。
ケの日では通り庭を経由して日常の時間を共有する。
ハレの日では冠婚葬祭、地域イベントを
開催し非日常を感じさせる。
通り庭の変形や動線の変化により同じ空間でも
ハレとケを明確に分ける計画とした。

不倫は文化なのか

家庭のあり方についてを見つめ直すことを脱家族と捉える
例えば、不倫です。不倫を肯定する訳でも否定するわけではないが不倫が絶対いけないこととは、断定ができない

なので、この7世代中では自由に真の姿を見せれるような、「公認不倫」を採用する場所を作る。



公認不倫を認めるメリット
不倫をすることで幸せオーラがでて家庭の問題が減る、
家族と恋愛は分けることにより大切さが増すなど、
色々メリットがある。

もちろんデメリットもあると思うが、
7世代の中で皆が家族のように相談や一緒に子育てをし、
ストレス発散ができる味方がいるということで
公認不倫も上手く進むと考えた

そこで、家族ですることはさせたいということから、
ご飯、お風呂、基本は一緒にとるように
共有のダイニングキッチン、大浴場を取り入れた

また、建物の形や配置にもこだわった
この7世代だけの特別空間を作りたいということから
囲った形にし、全てのLDKから他のLDKが覗け、
他所の家族と自分の家族を比べることにより
「隣の芝は青くみえる」日本人の特徴の幸せに見られるような見栄張りから、
家族を大切にすると考えこの設計とした



1階平面図



2階平面図



愉快的先輩達



三本釣りトリオのあゆ

役職 ゼミ長

子分 オーガ鯖

カンシロウ

圧倒的リーダーシップで17期を率いてきた姉御、しかしたまに抜けてる性格で場を和ます。たまに来る差し入れありがとうございます。



一矢報いるso low

役職 副ゼミ長

子分 廃ブリッジゆずき

親しみやすさの塊のムードメーカー。子分に頭が上がらない時もあるがいざとゆう時に頼りになったりならなかったりする。また新居に押しかける予定を計画中。



お花見カーリング

役職 イベント

子分 ドリーム歩夢

にじさんとキヨが大好きな女子。静かに変なことをしてた気がするChroNoiRのパベを持ち歩き今日も街を闊歩する。



おとととノリコ

役職 企画

子分 カモンめぐみ

米利休

後輩に振り回された苦労人。卒制では迷惑をかけた人がいるらしい。でも、なんか仲良く飲みに行ったこともあるのでなんだかんだ良い人の優しい先輩。



オニオンリングみわ

役職 美化

子分 森の中のこうちゃん

賑やかな17期を静かに見守るお姉さん。同期にも好かれながら下にはこうせいを従えながらギリギリまで巨大な模型制作に励んでいたしっかり者。



Mt.高野豆腐

役職 会計

子分 エスプレッソゆうと

真面目なしっかり者、しかし最初に見せられたのはお酒で潰れてる動画でした。そんなお茶目な可愛い先輩、しかし、裏には何かを隠し持つ静かなるドン。



平田フライパン

役職 広報

子分 ソ・ウシウシ

極度の人見知りらしいが、18期の推しに負けカラオケやラーメンによく行き、イチローと共に仲良くなった先輩。東京で友達はできたんだろうか...



模型ブレイカーひな

役職 広報

子分 horry

圧倒的な酒の弱さ、いつの間にか赤くなって酔ってたイメージしかない。卒制期間は自分の机より他の人の机にいたことが多かった問題児。しかし、人の良さと明るさに惹かれる人もいそうらしい。



税込
二〇〇〇ノマー

野間ゼミ HomePage



野間ゼミ Instagram



なにこれ？バーコードです。
©2020 野間ゼミ

